



① ファサード正面図 ELEVATION S=1/30

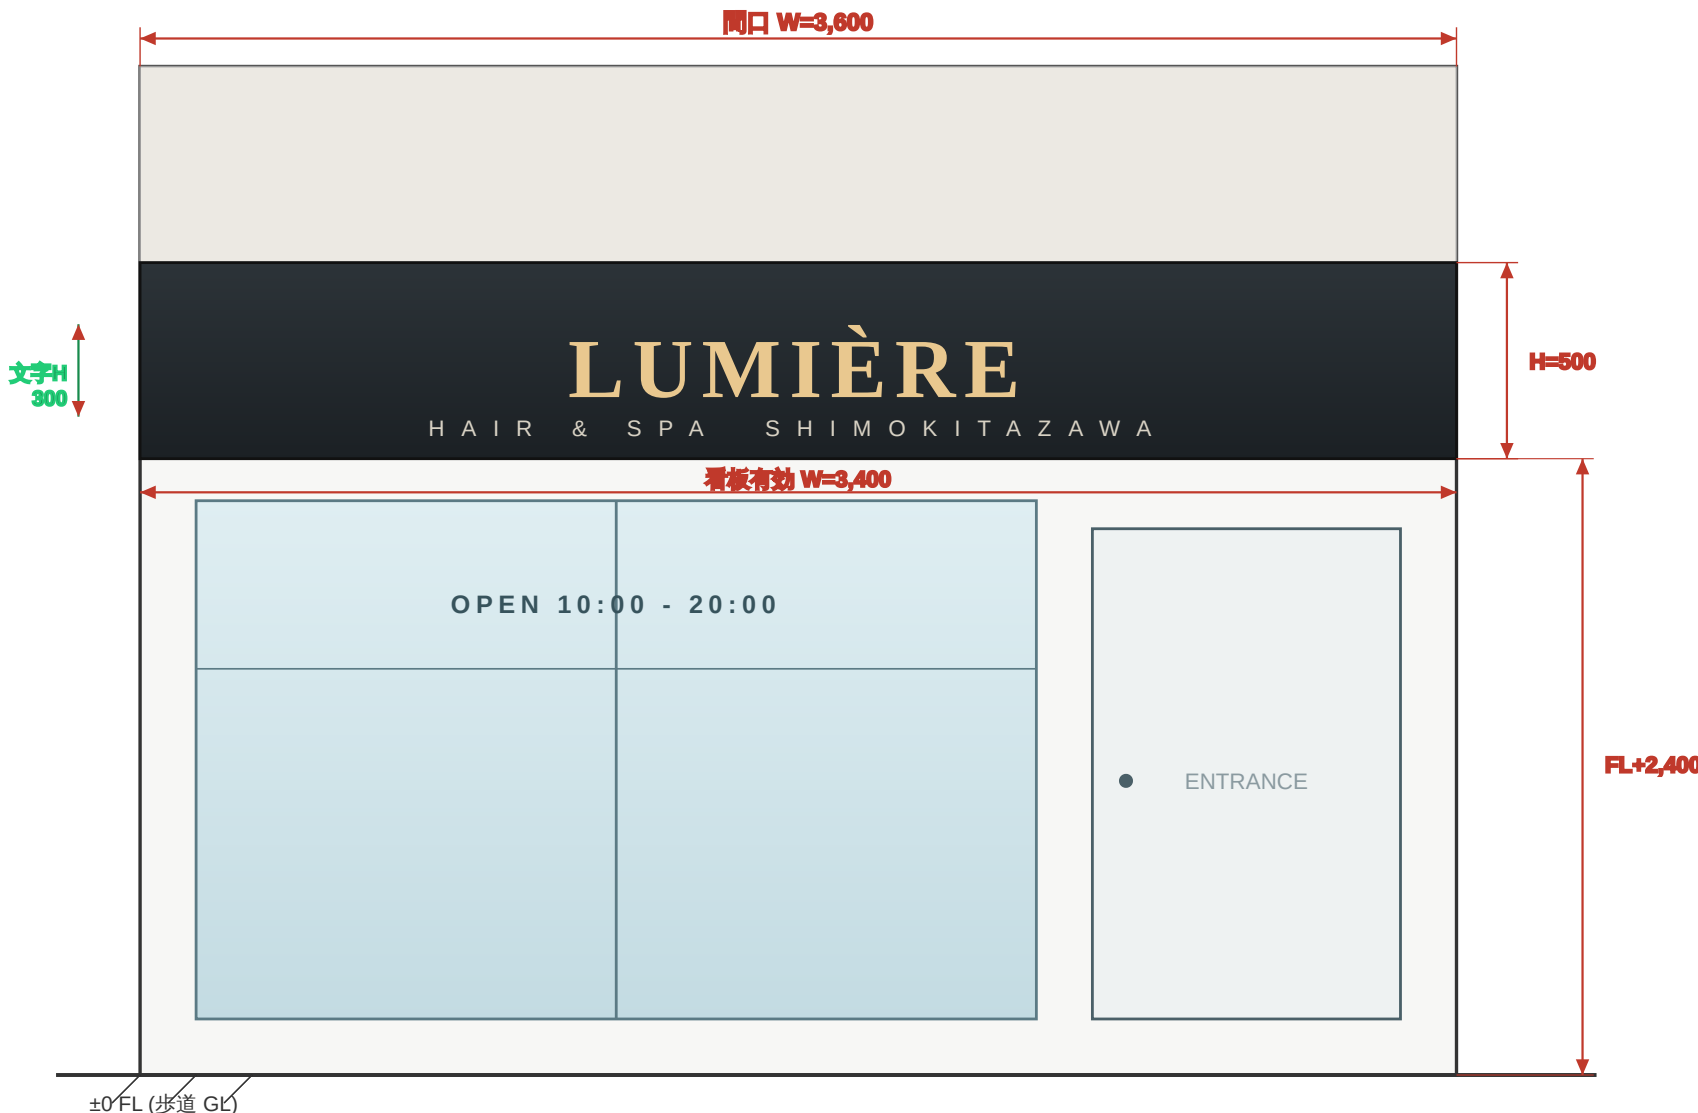

② 仕様表 SPECIFICATION

看板種別	ファサード（正面）看板 / チャンネル文字 LED内照式
ベース板	アルミ複合板 t=3mm（ボンデ鋼板下地） / ロゴ・店名切文字取付
文字仕様	ステンレスチャンネル文字 H=300 / 表面アクリル乳半 / 内部 白色LEDモジュール
仕上げ	■ ベース：マットブラック焼付塗装 ■ 文字：シャンパンゴールド
寸法	W3,400 × H500 × 奥行 D60（文字投げ D40）
取付高さ	看板下端 FL+2,400（有効天井下 200 クリア）
取付方法	壁面アンカー M8@600 + アルミアングル下地 / 4点固定
電源	AC100V 専用回路 / 消費電力 約120W / タイマー連動点灯

③ 取付断面詳細 SECTION S=1/6

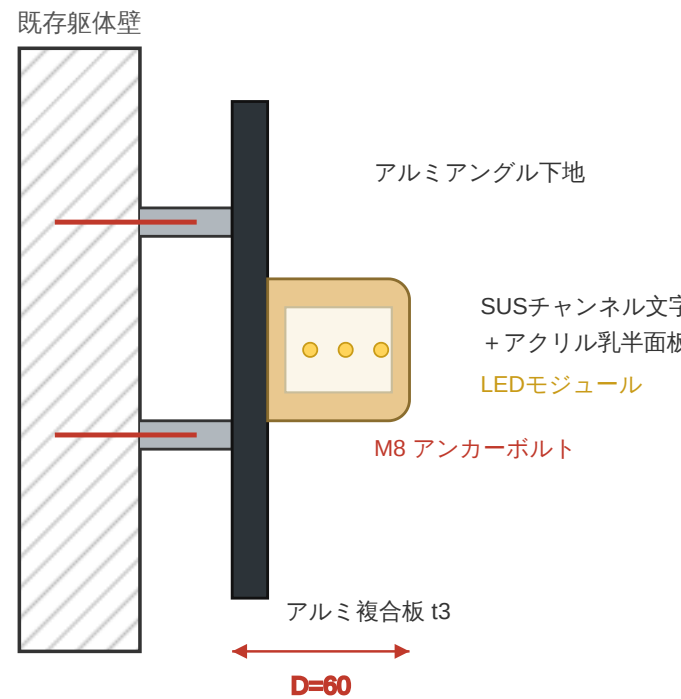

下北沢 内装工事

Hair & Spa "LUMIÈRE" / 店舗サイン計画

所在地
東京都世田谷区北沢（下北沢駅 至近）

作成日
2026-07-18

用途
美容室 / サロン

作成
Takuya Okada

縮尺
S=1/30・1/6 (A3)

承認
—

単位
mm

Rev.
A

看板図面

図番 SN-01 / ファサードサイン